
PROJET 3 : HABITER TRAVAILLER

REFERENCE


LA MAISON POLI, PEZO VON ELLRICHSHAUSEN, CHILI, 2005



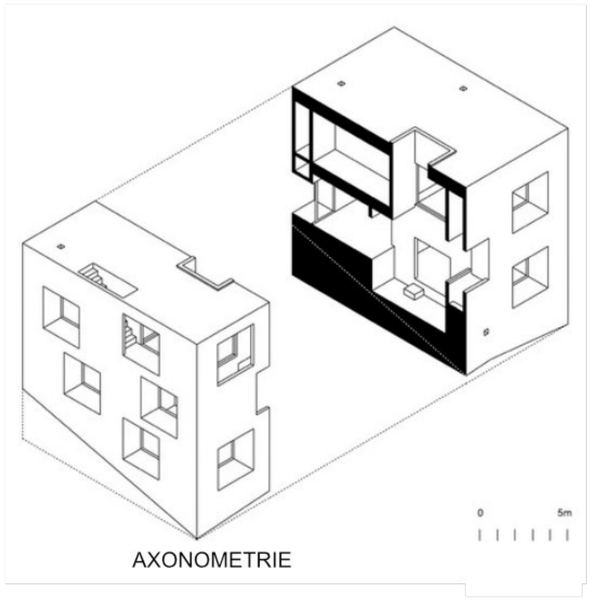

AXONOMETRIE

LINO TAGLIAPIETRA : ARTISTE VERRIER VÉNITIEN, NÉ EN 1934

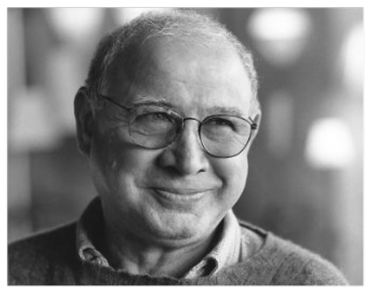




ŒUVRE DE LA SERIE LONDON, 2018




ŒUVRE DE LA SERIE PETRA, 2011


SITE

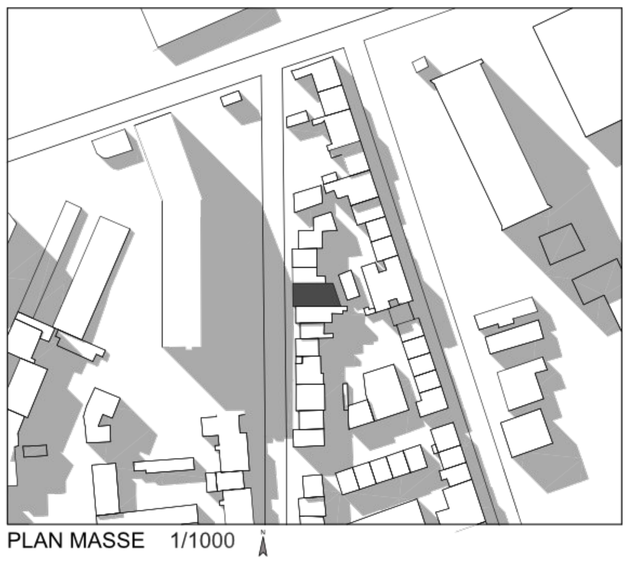


PLAN MASSE 1/1000

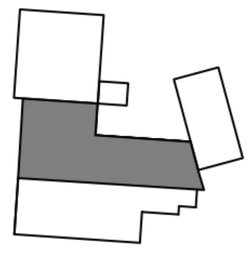


EMPRISE CONSTRUCTIBLE - R+1

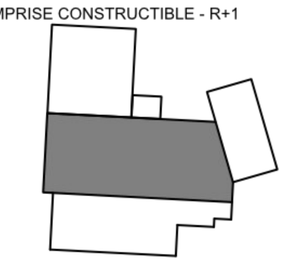

EMPRISE CONSTRUCTIBLE - RDC

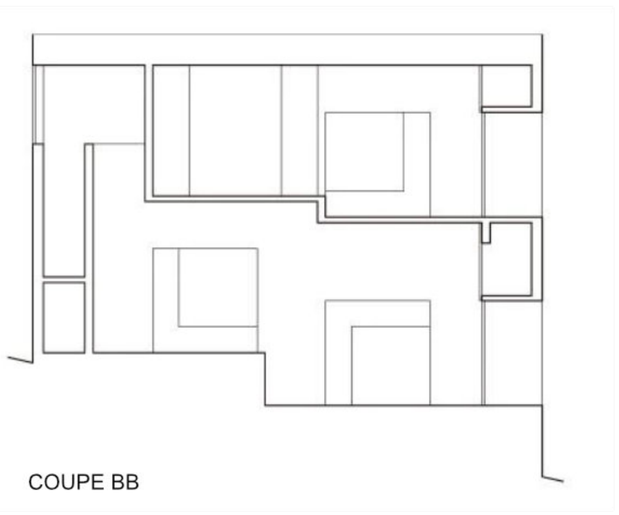


COUPE BB

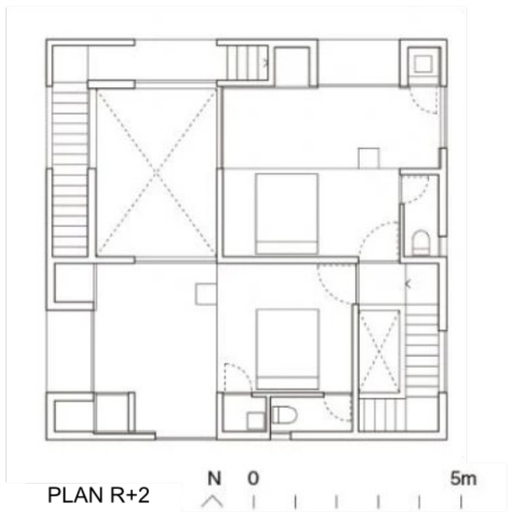



PLAN R+2


INTENTIONS

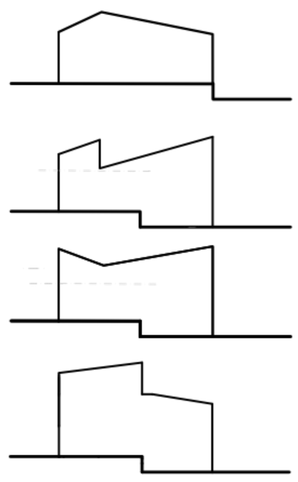


CROQUIS

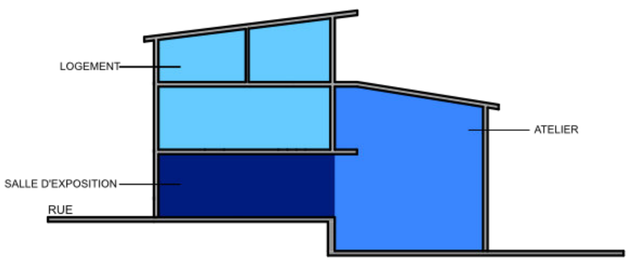

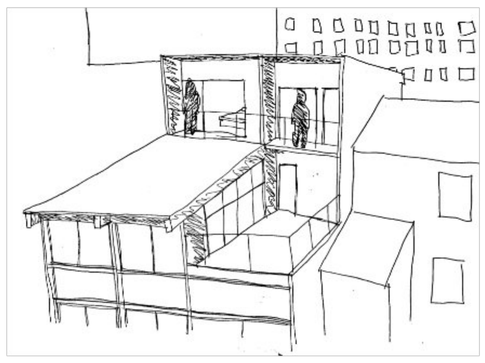

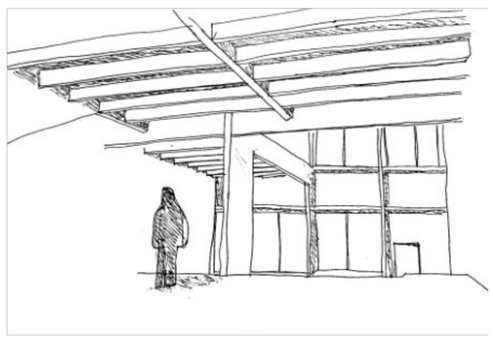

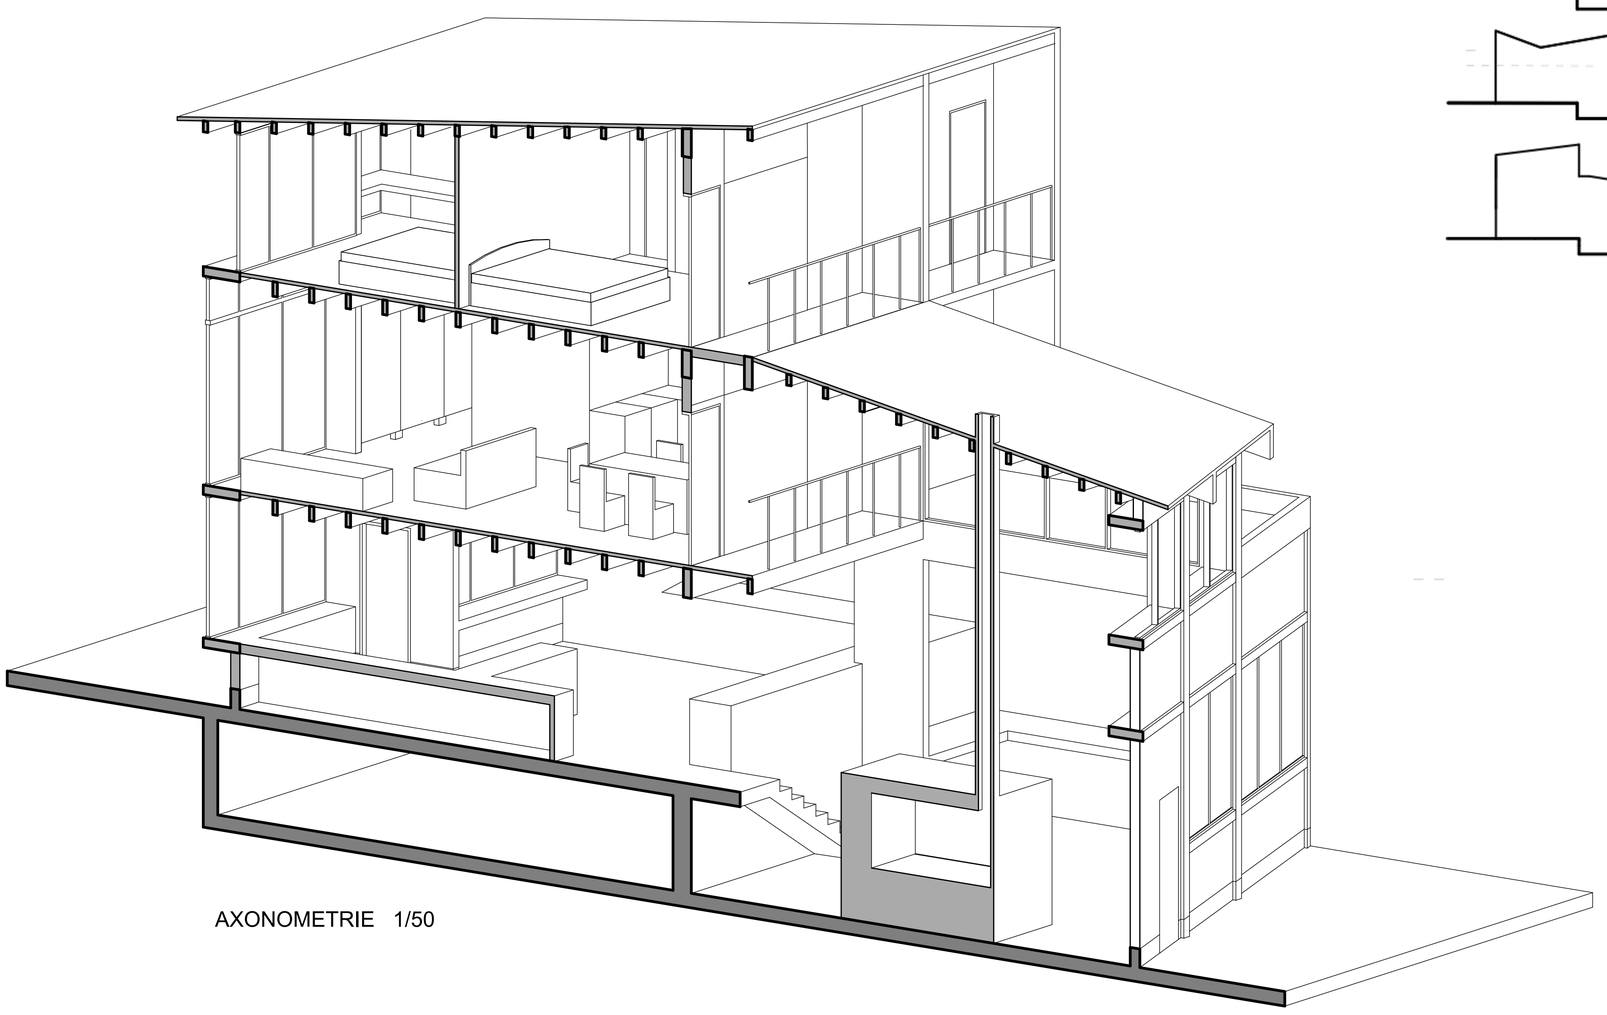



AXONOMETRIE 1/50

RENDUS 3D






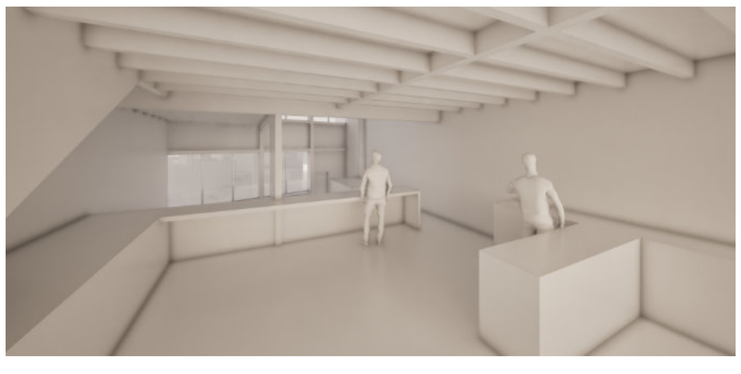

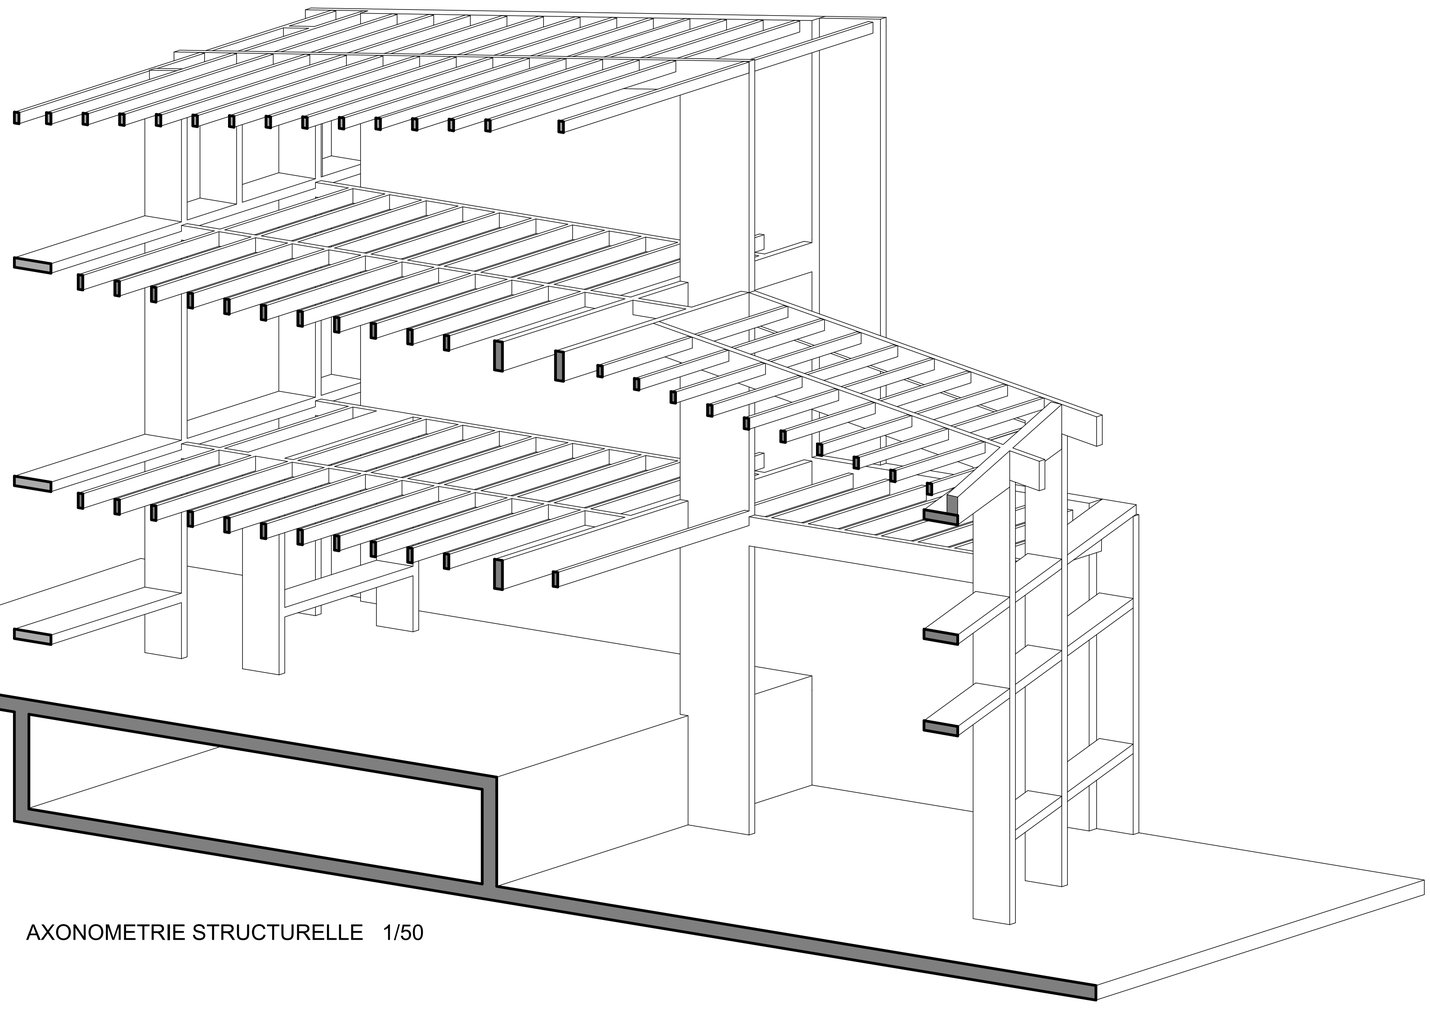

AXONOMETRIE STRUCTURELLE 1/50

LEVI GOLDSCHMIDT
JEAN-FRANCOIS MONNIER
SIMON BAUCHET
G4

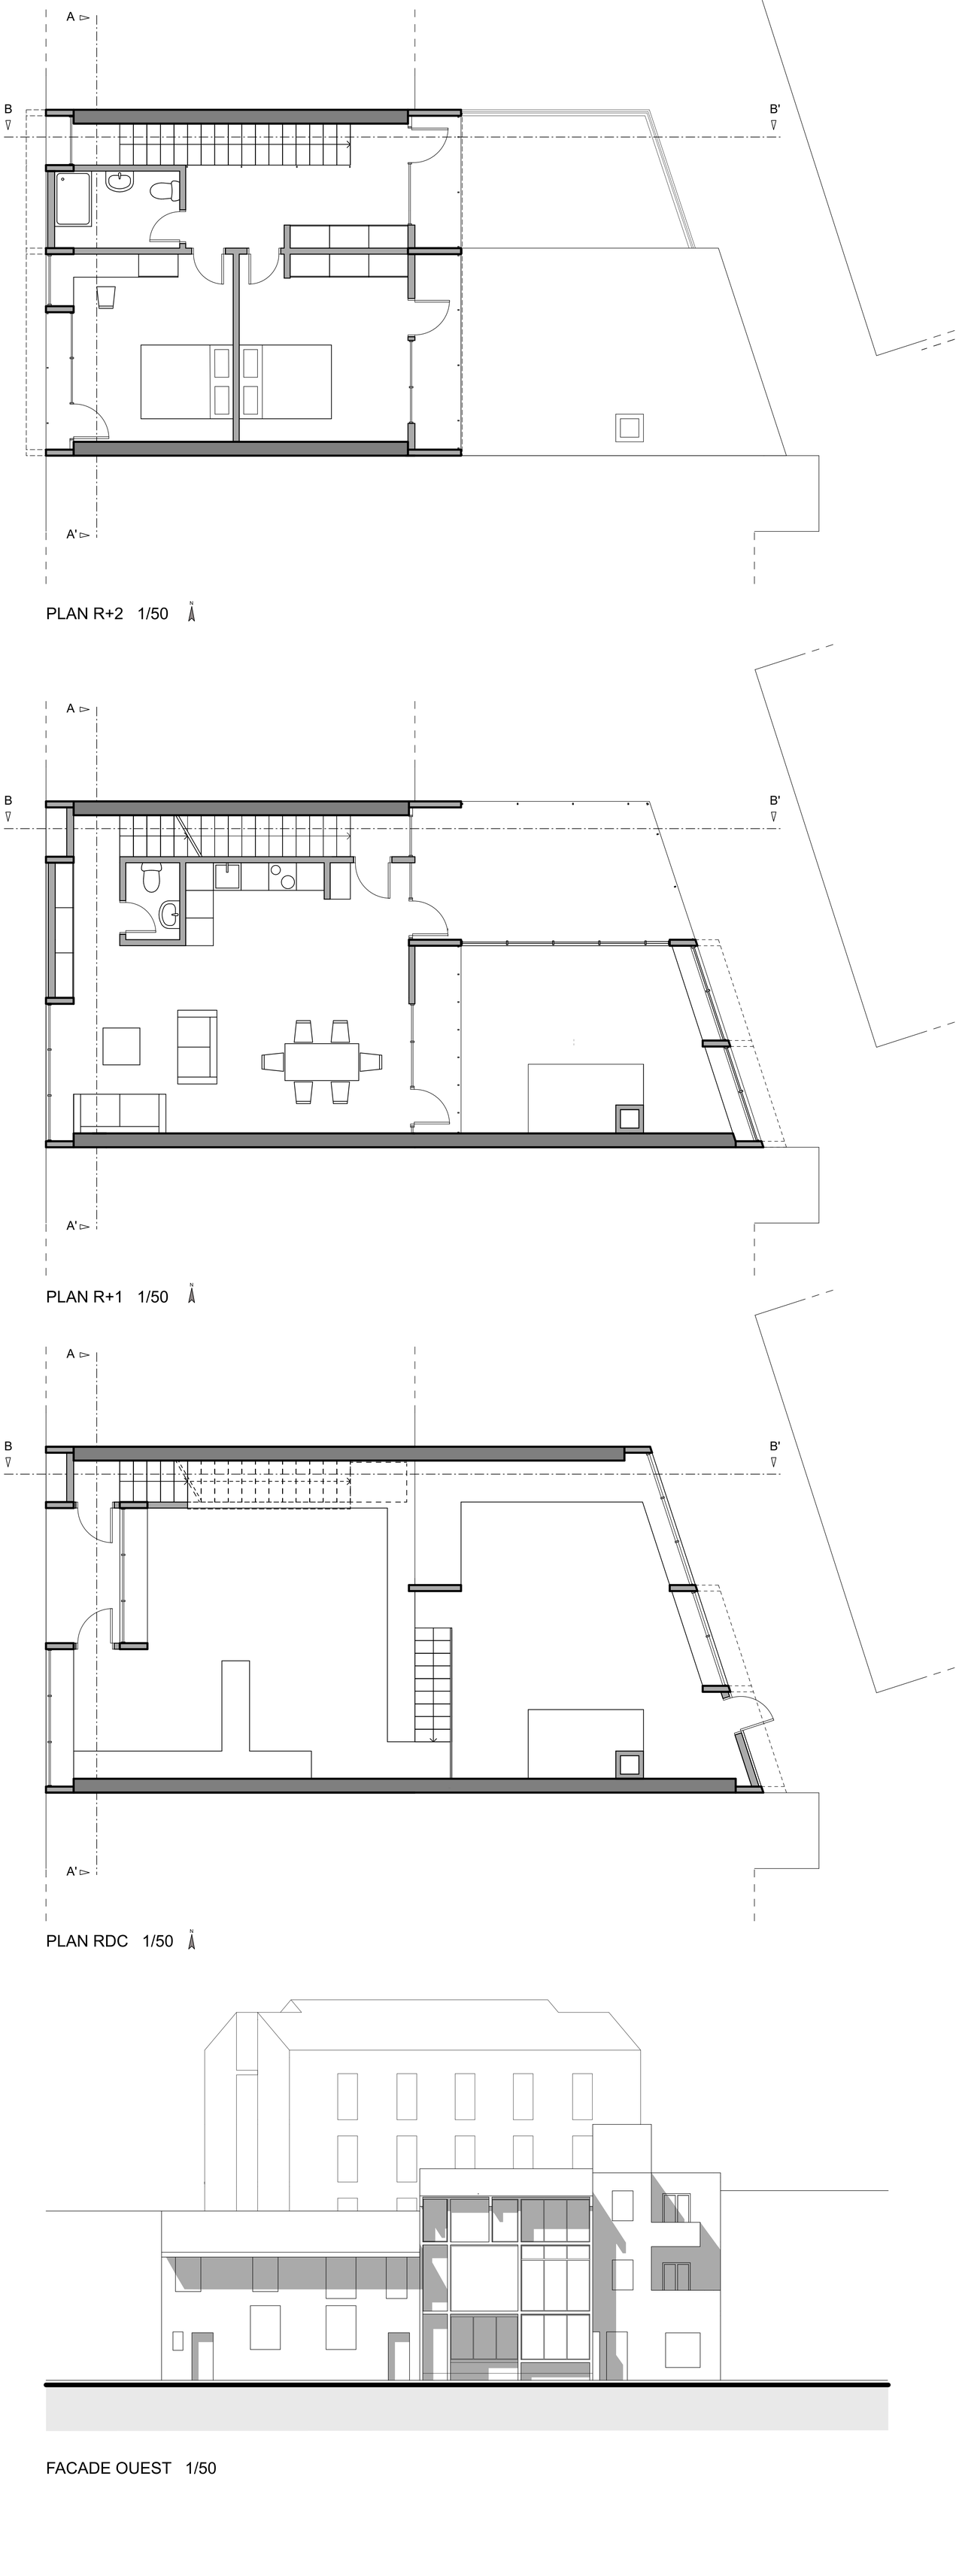


PLAN R+2 1/50


PLAN R+1 1/50

PLAN RDC 1/50


FACADE OUEST 1/50

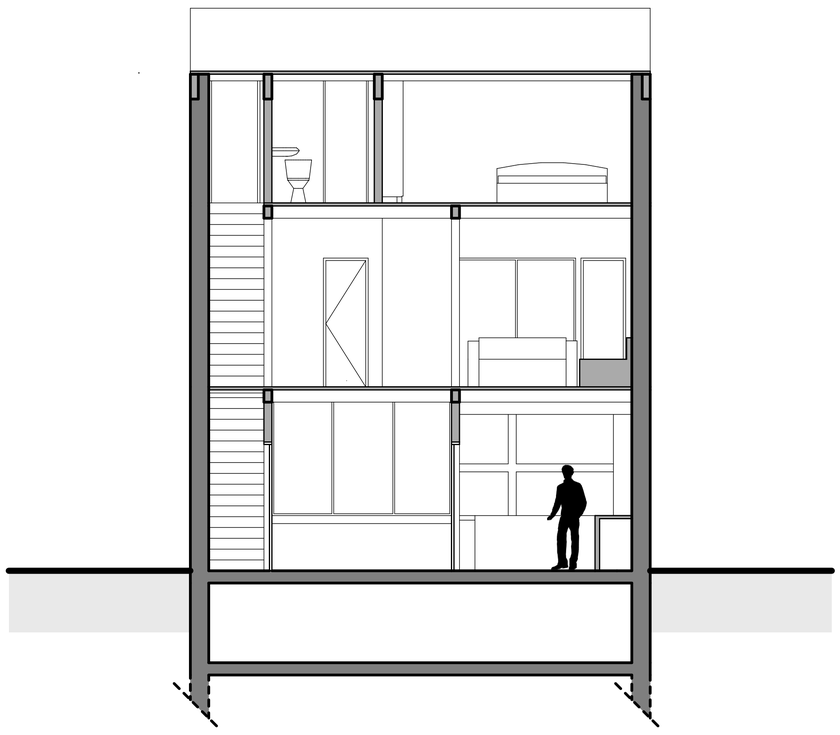

COUPE AA' 1/50

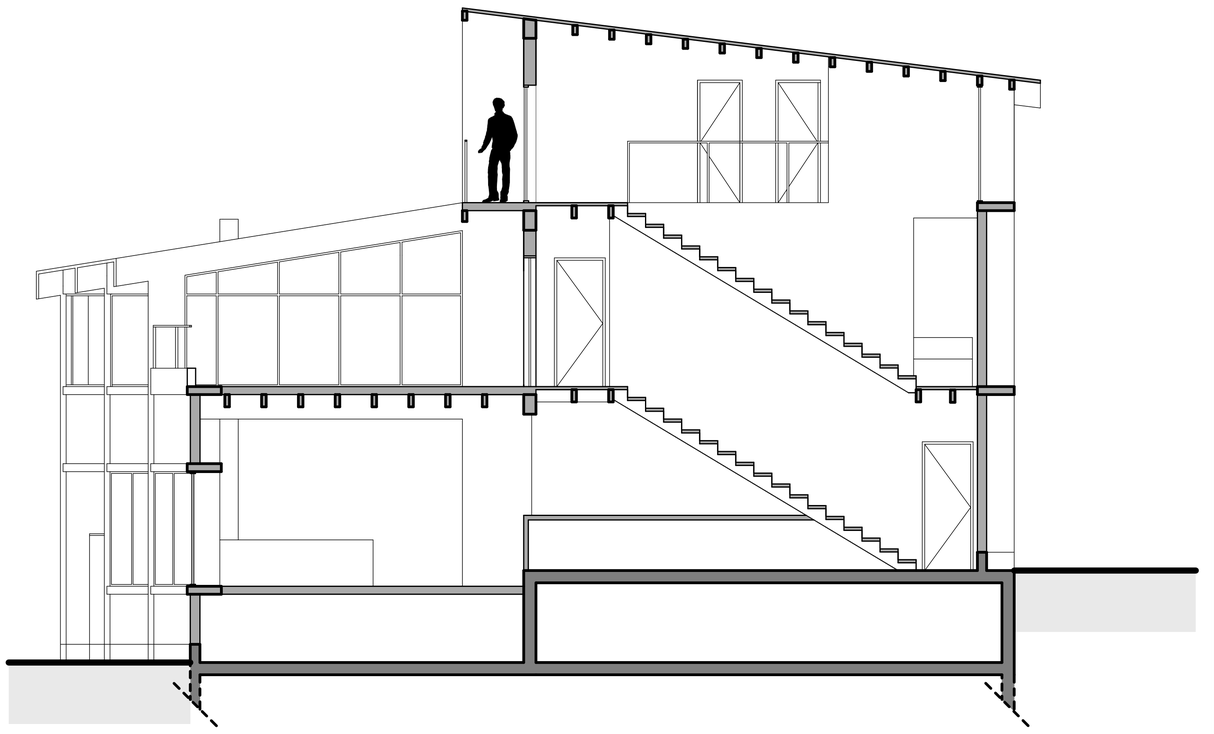

COUPE BB' 1/50

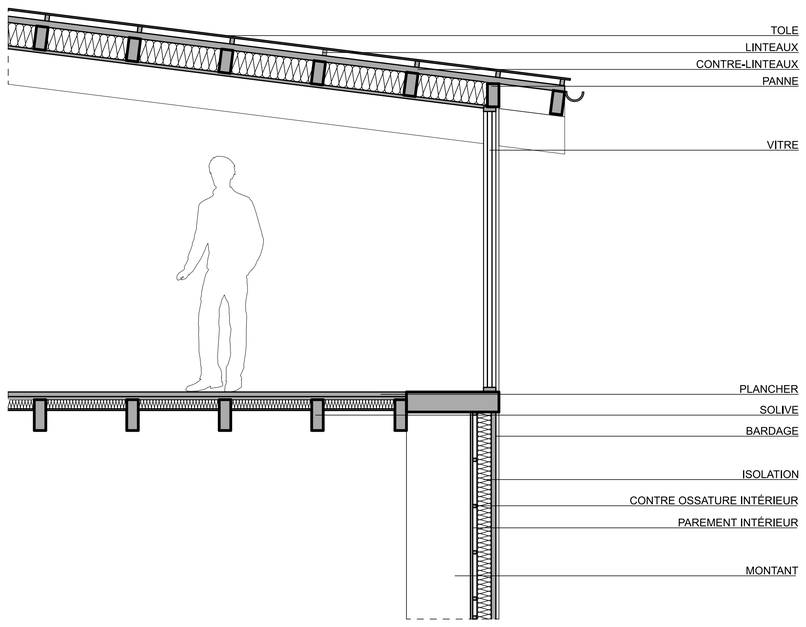

COUPE DÉTAILLÉE 1/20



FACADE EST 1/50

LEVI GOLDSCHMIDT
JEAN-FRANCOIS MONNIER
SIMON BAUCHET
G4